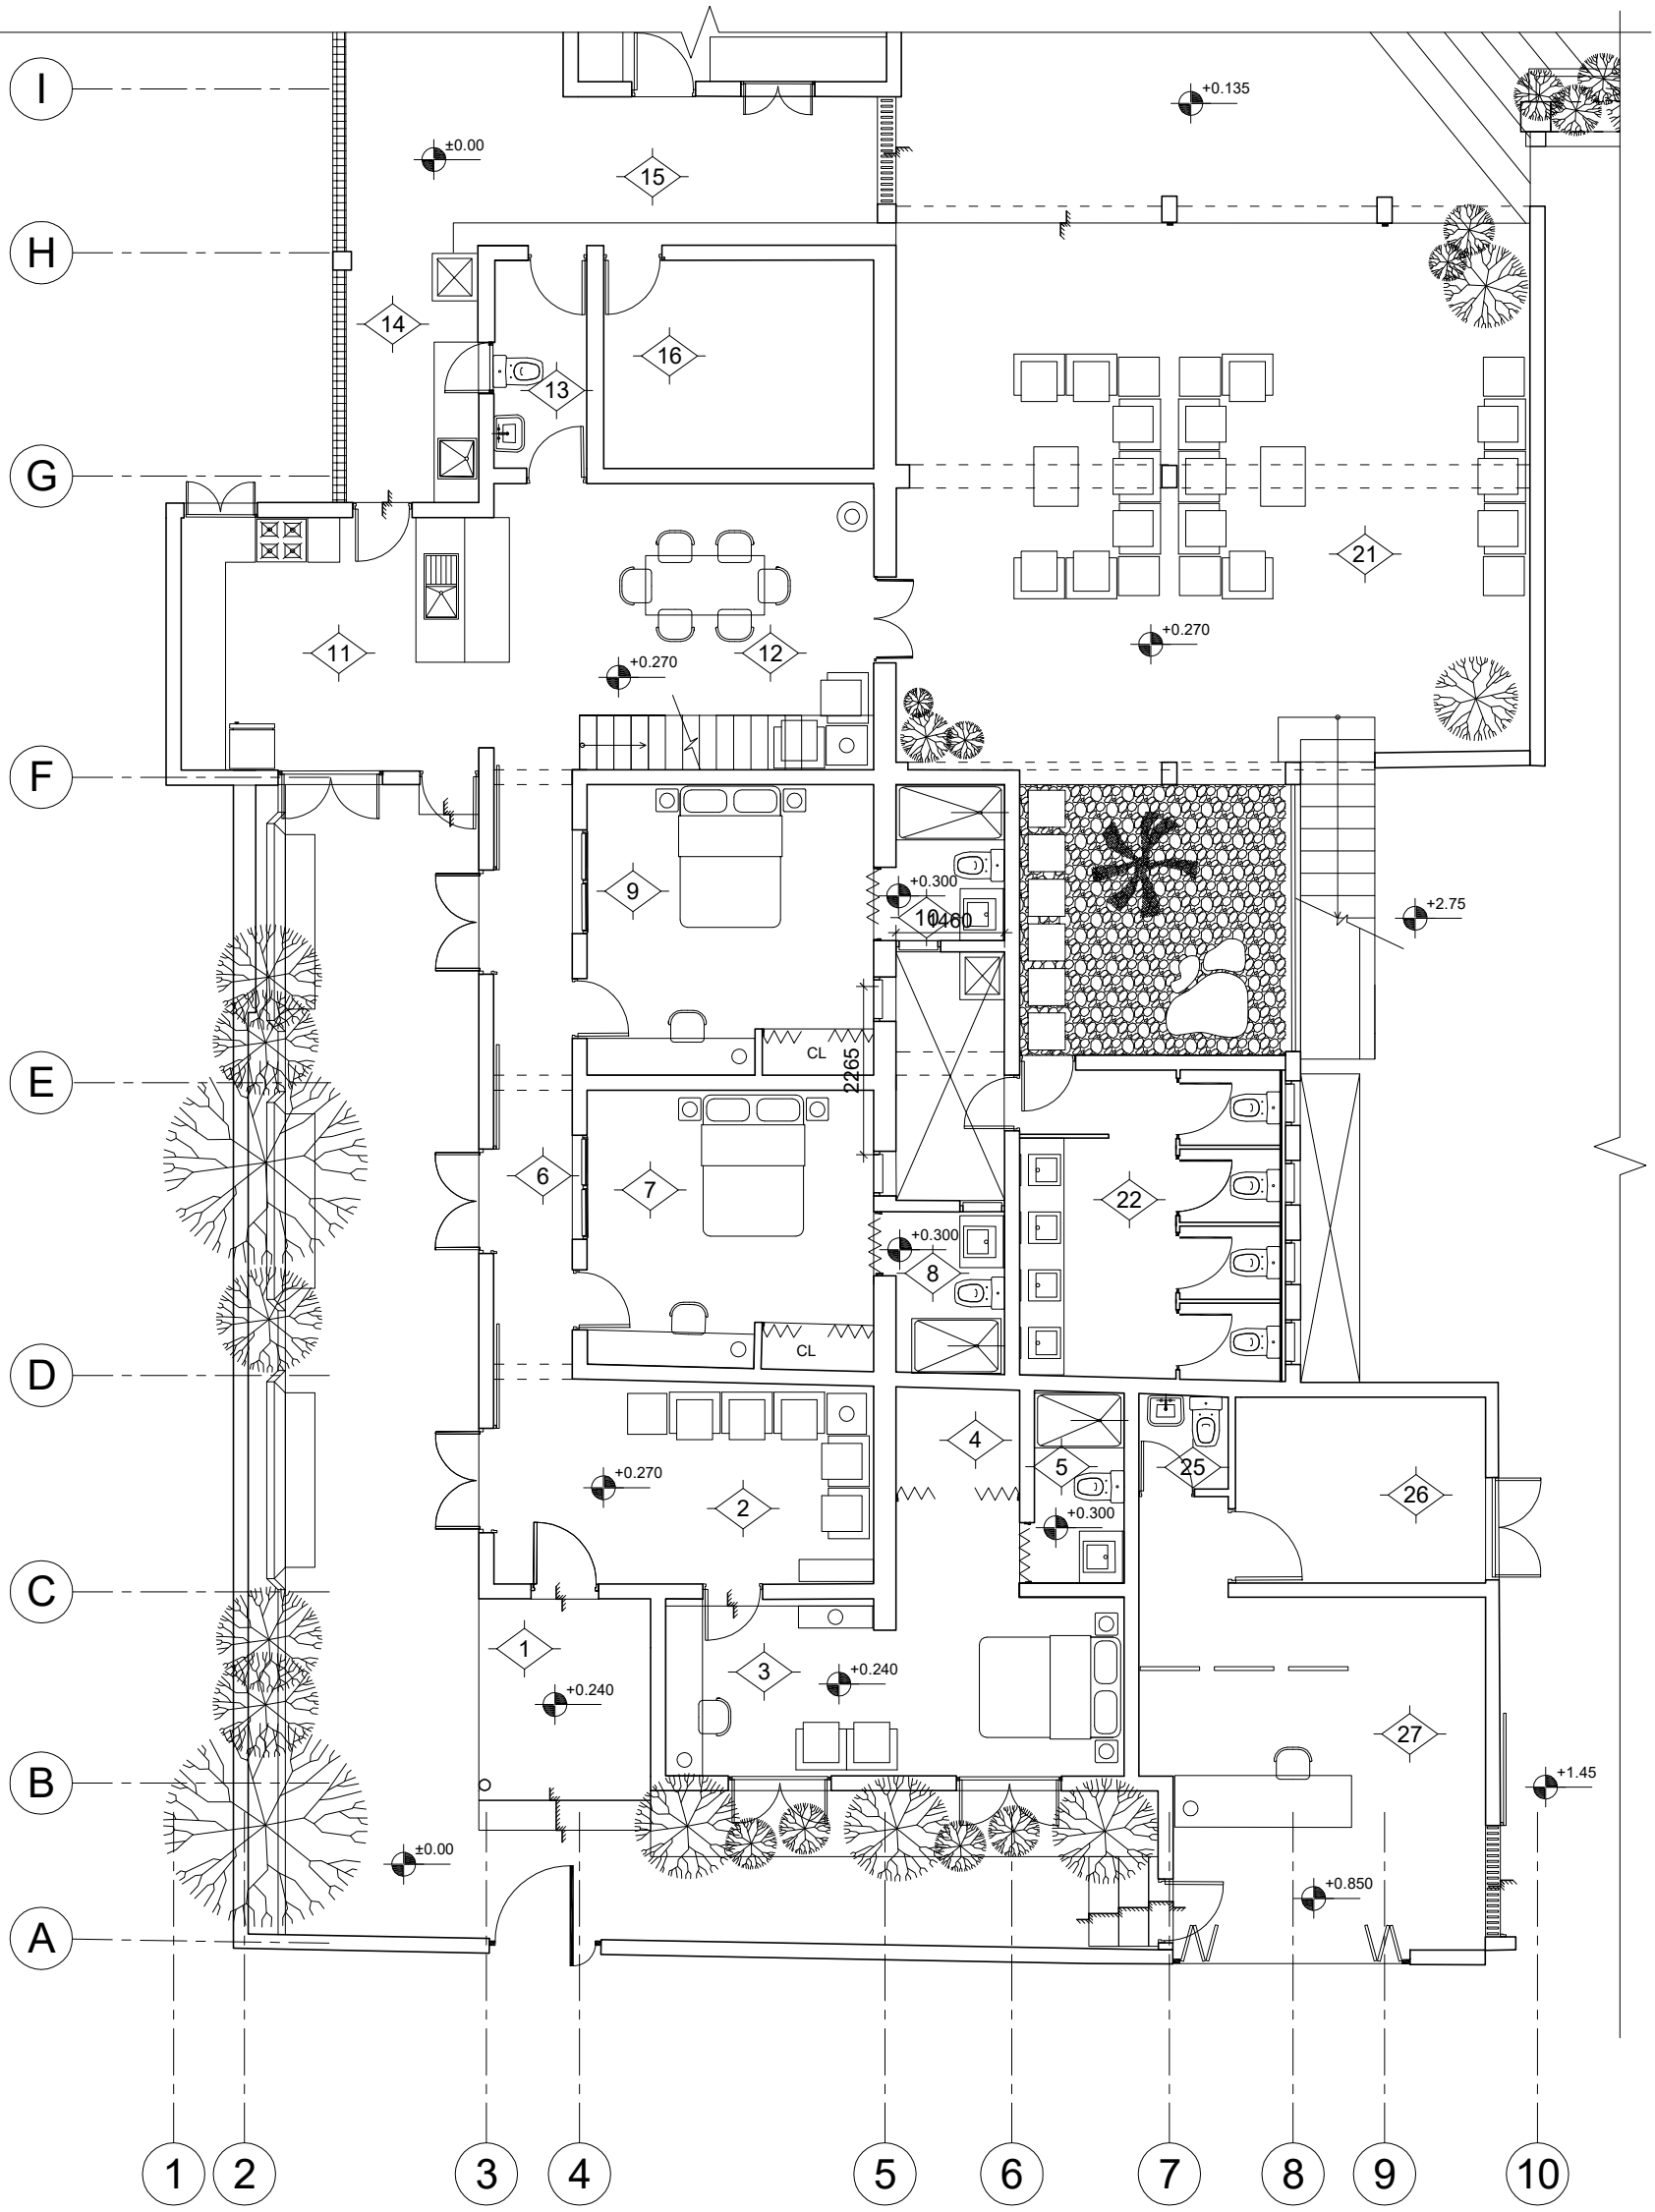


SUPERFICIE ÚTIL		
No.	Descripción	Área (m²)
1	Portal	6.26
2	Estar	13.91
3	Habitación de Maestros 1	16.62
4	Vestidor Hab. Maestros 1	2.70
5	Baño Hab. Maestros 1	3.16
6	Pasillo de Circulación	8.67

7	Habitación de Maestros 2	14.36
8	Baño Hab. Maestros 2	3.16
9	Habitación de Maestros 3	15.03
10	Baño Hab. Maestros 3	3.07
11	Cocina Casa de Maestros	14.70
12	Comedor Casa de Maestros	19.19
13	Baño Casa de Maestros	3.49
14	Patio de Servicio Casa de Maestros	6.08

15	Pasillo de Circulación 2	17.06
16	Almacén de Insumos	10.10
21	Vestíbulo de CASA LUZ	80.89
22	Servicio Sanitario Público	8.67
25	Baño de Recepción	1.53
26	Cuarto eléctrico para paneles	8.40
27	Recepción CASA LUZ	22.64

CASA LUZ/ Proyecto Ejecutivo/ Casa de Maestros PB/ Arquitectura/ ESC. 1/100 **A-02**

A3