
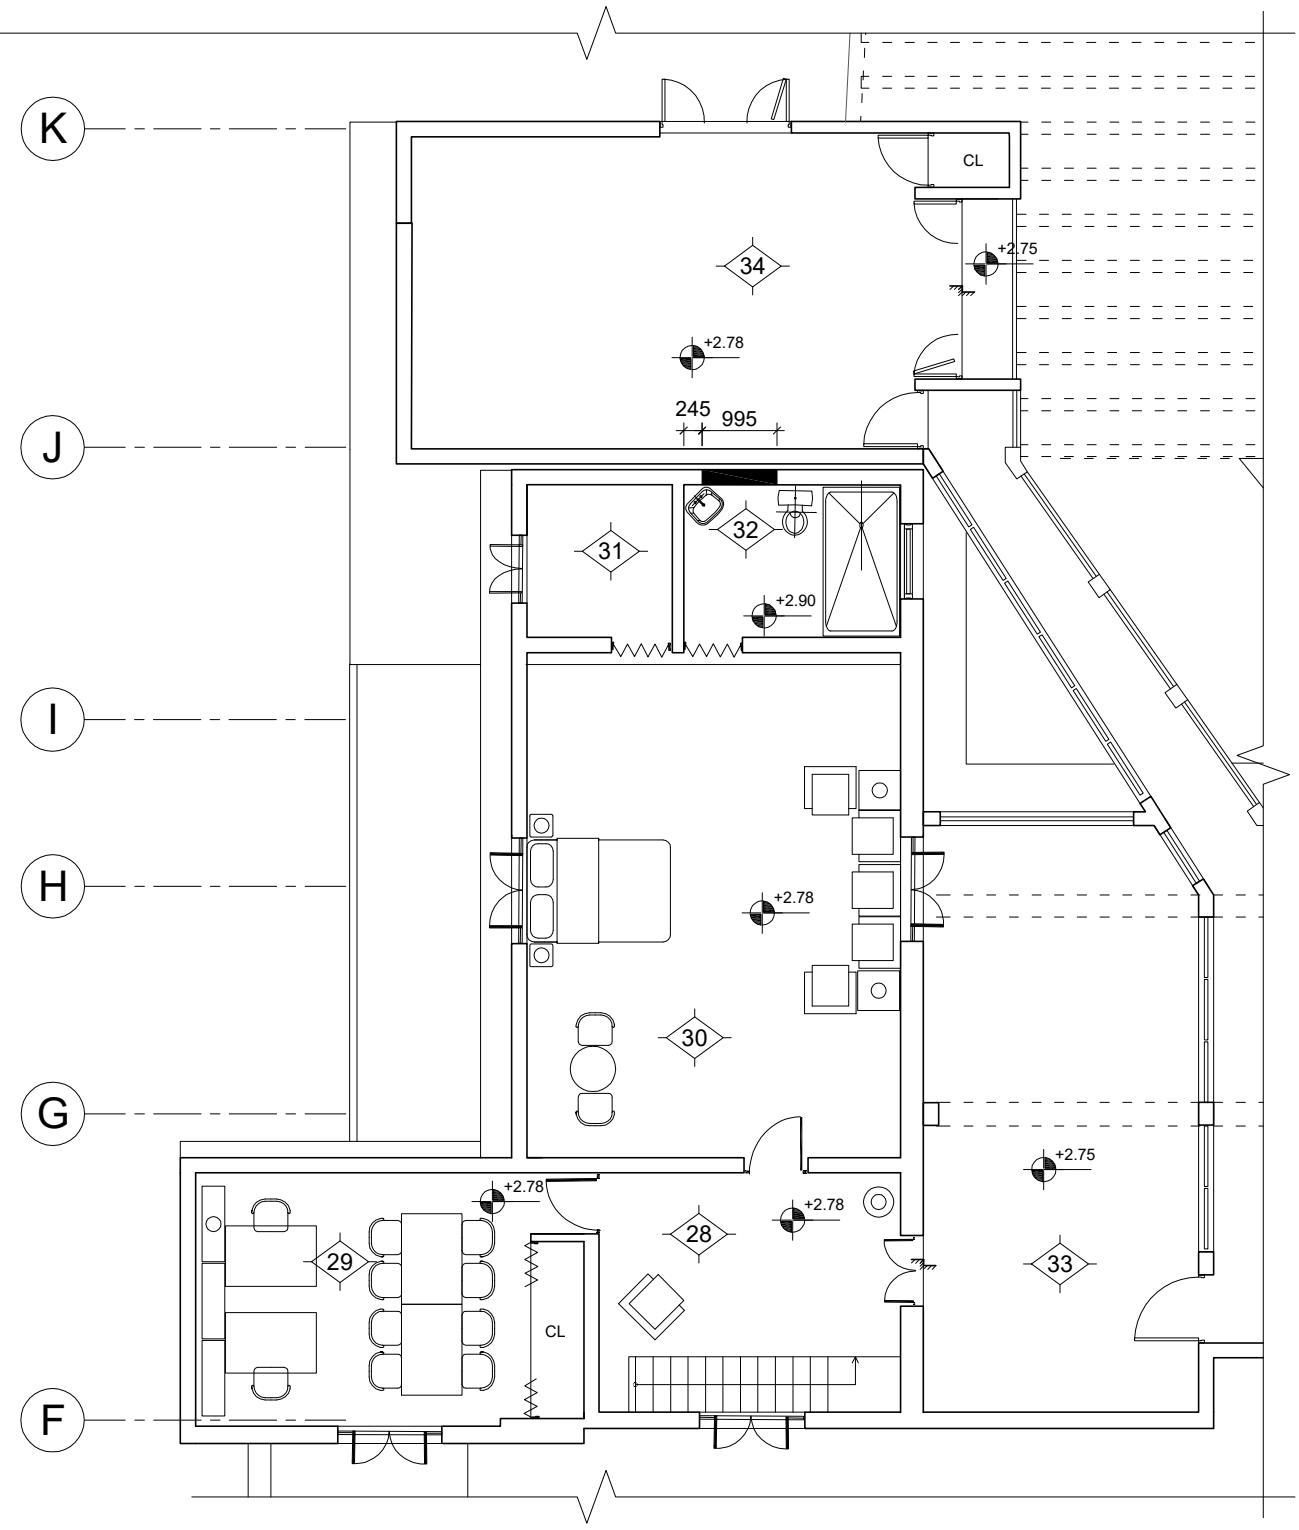


PLANTA ALTA. CASA DE MAESTROS Y AULA

SUPERFICIE ÚTIL		
No.	Descripción	Área (m²)
17	Cocina Comunitaria	14.13
18	Cisterna Casa de Maestros	11.34
19	Cafetería	25.23
20	Área de Mesas/Comedor	67.35
28	Vestíbulo Distribuidor	9.98
29	Oficina	16.99
30	Habitación Maestro Principal	32.96
31	Vestidor de Hab. Maestro Ppal	3.95
32	Baño de Hab. Maestro Ppal	5.83
33	Terraza de Hab. Maestro Ppal	27.63
34	Aula (Gong)	29.92

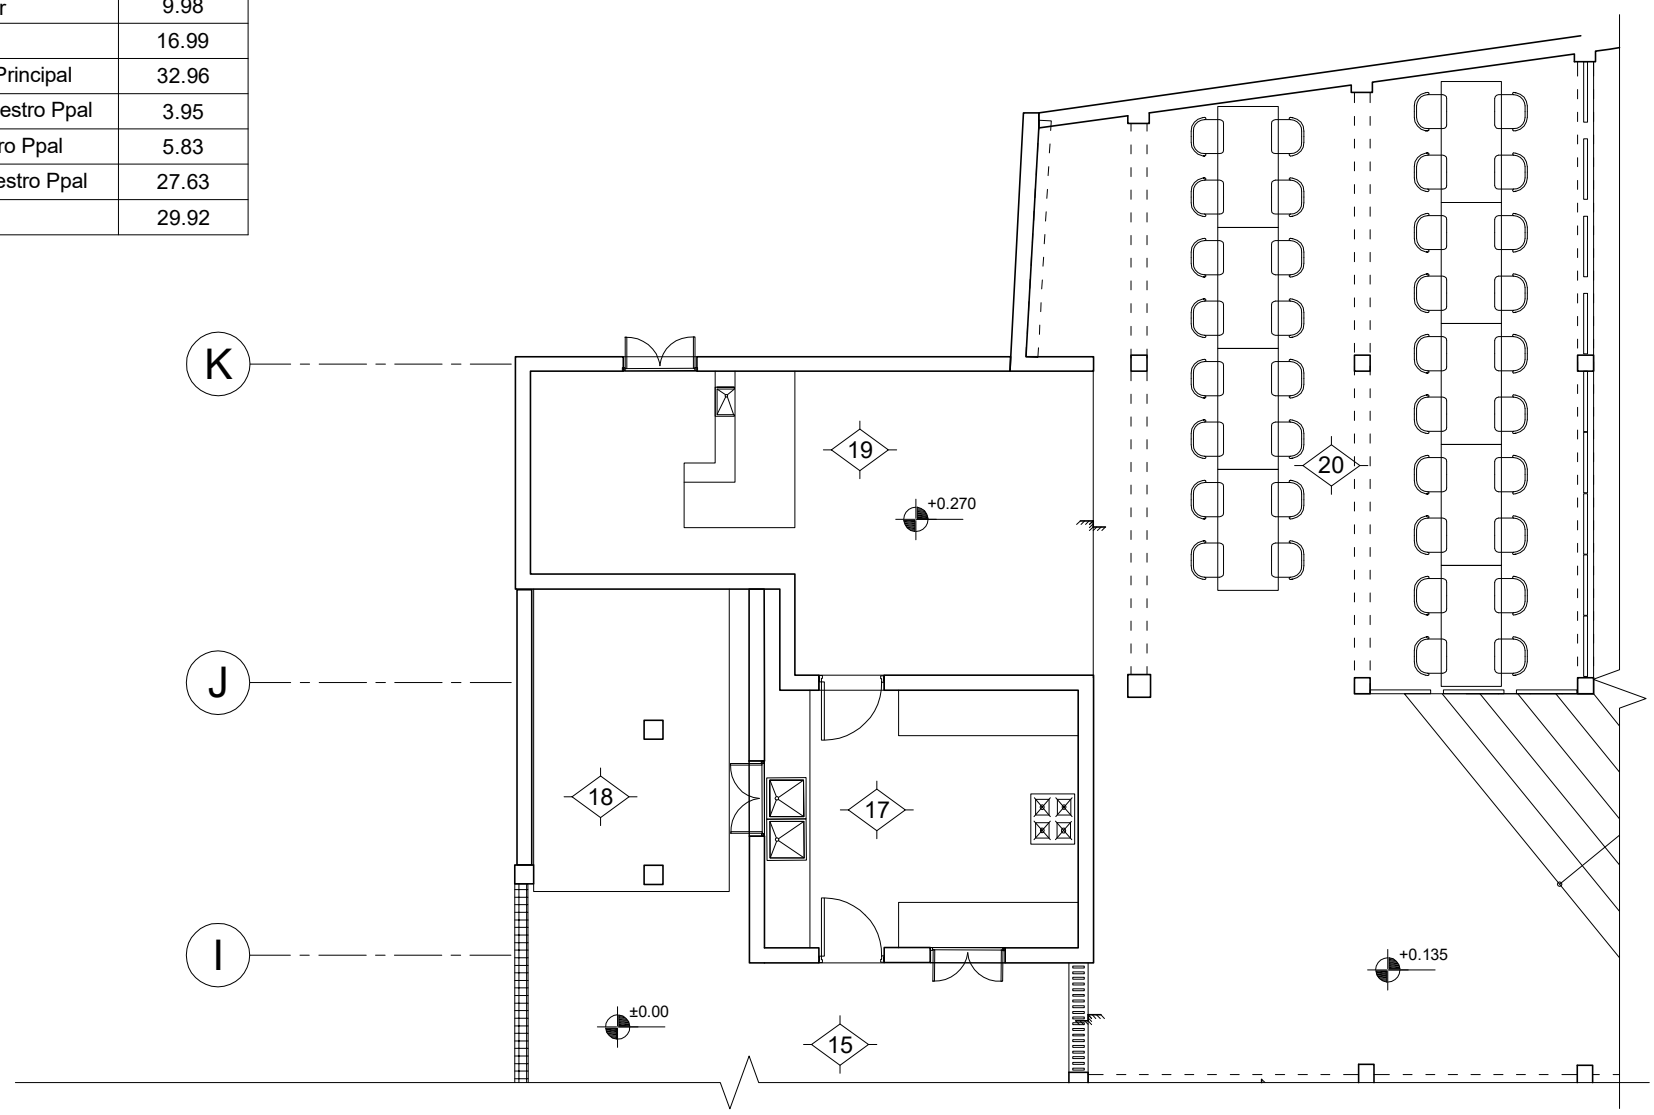

PLANTA BAJA. COCINA COMUNITARIA

CASA LUZ/ Proyecto Ejecutivo/ Casa de Maestros PB y PA/ Arquitectura/ ESC. 1/100 A-03